




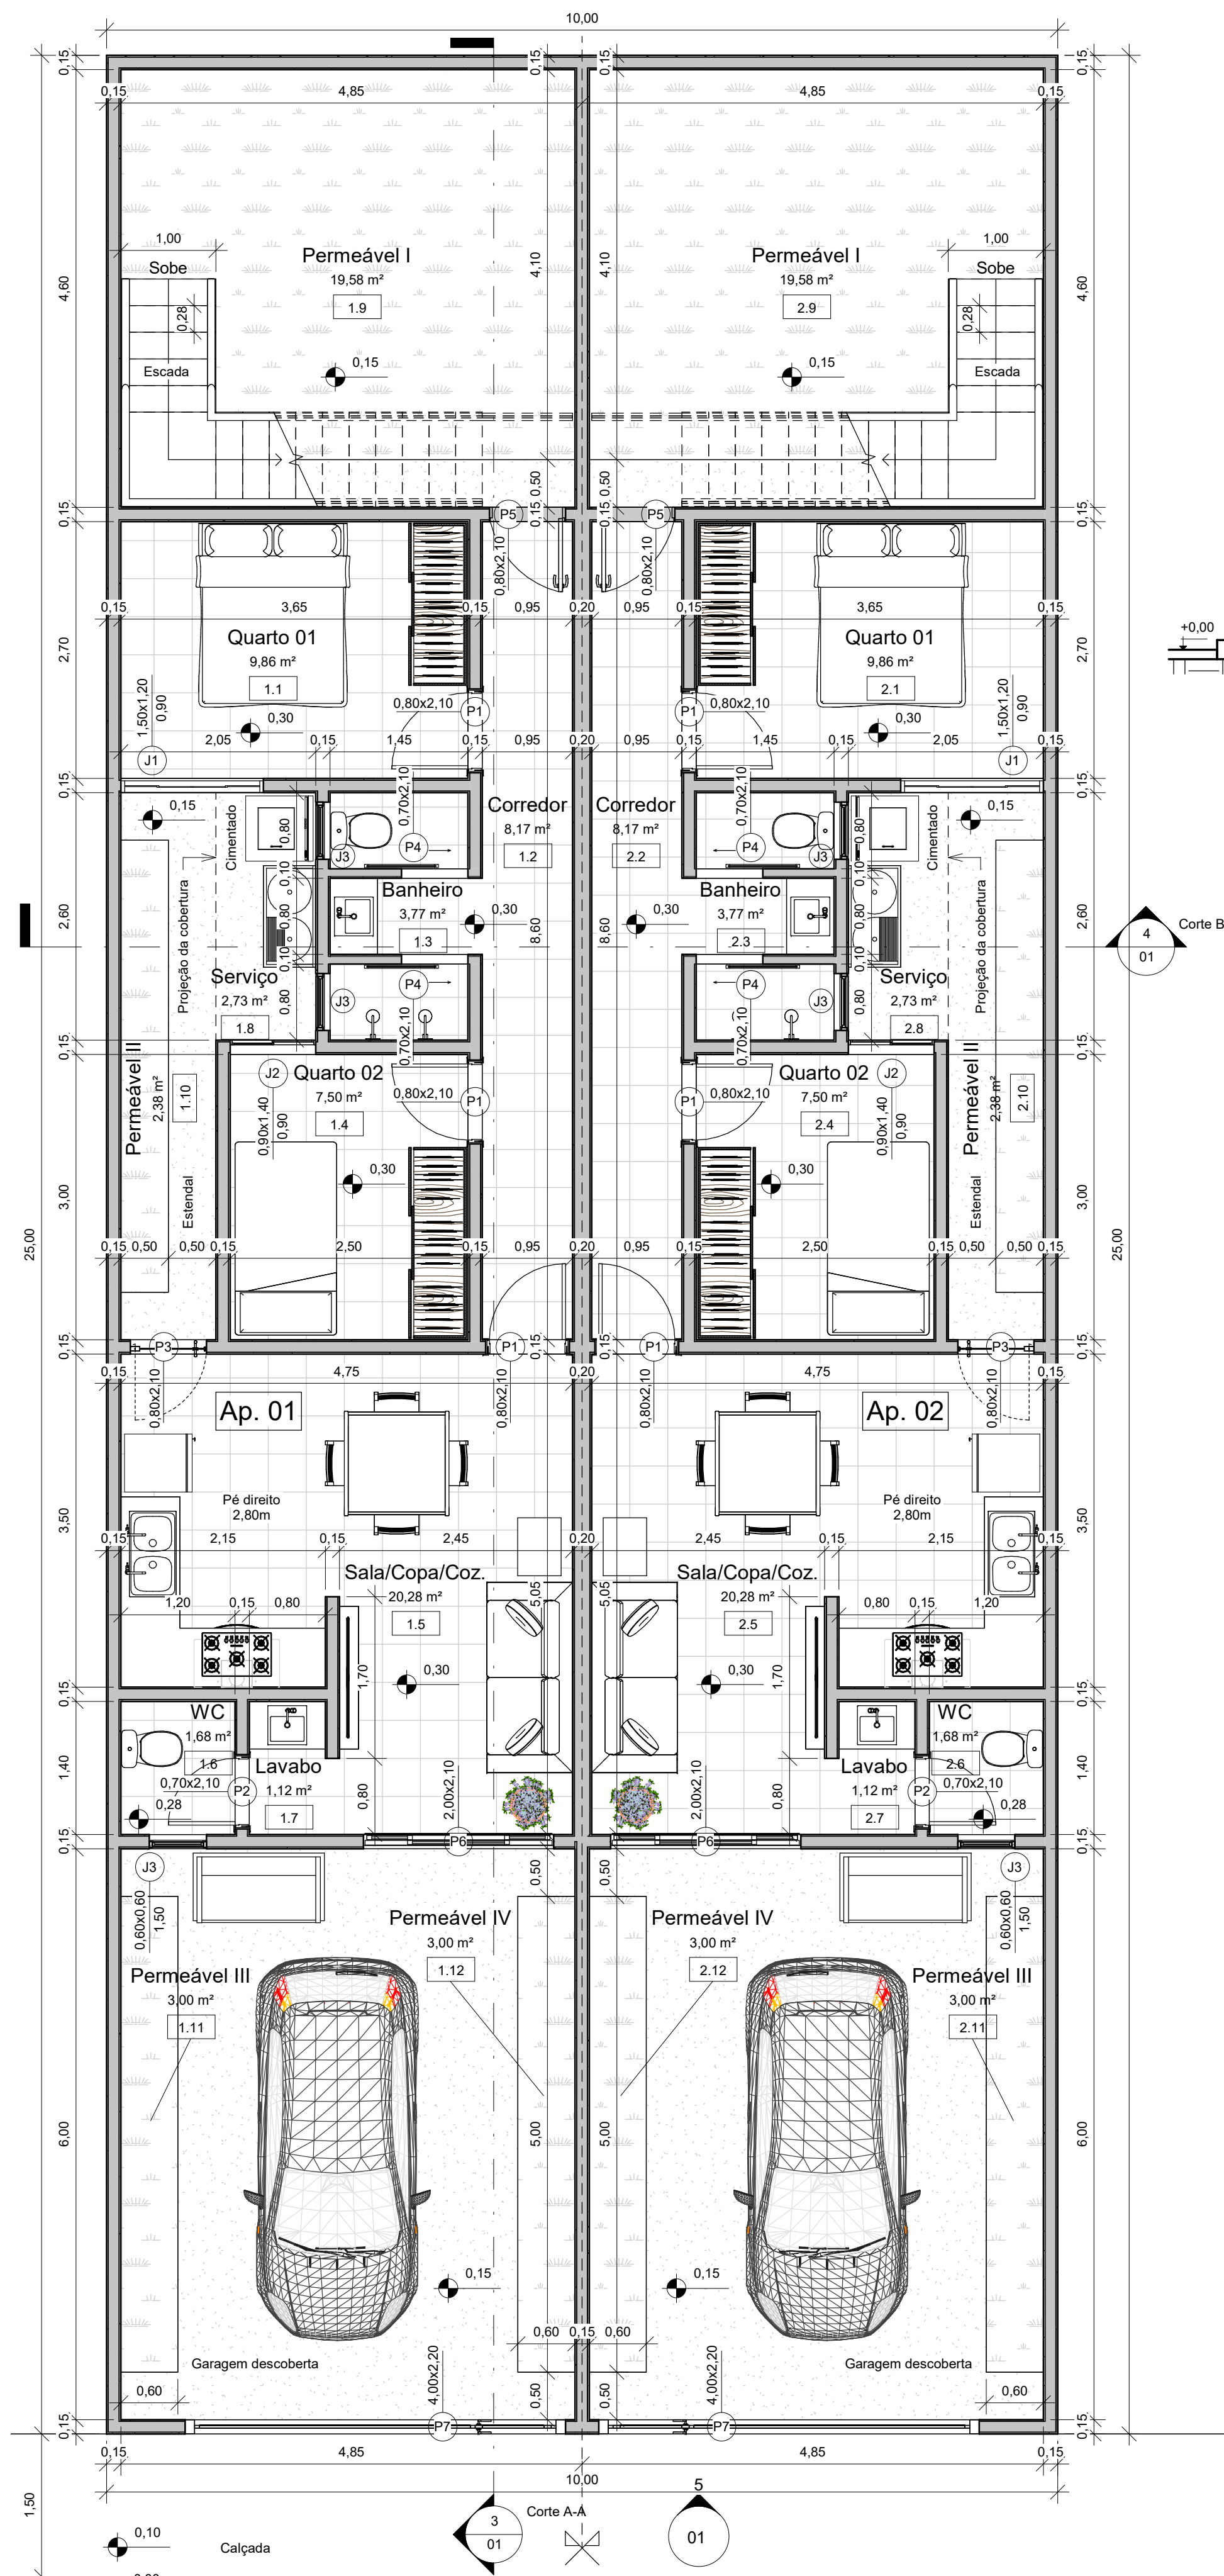

1 Pav. Térreo
1 : 50

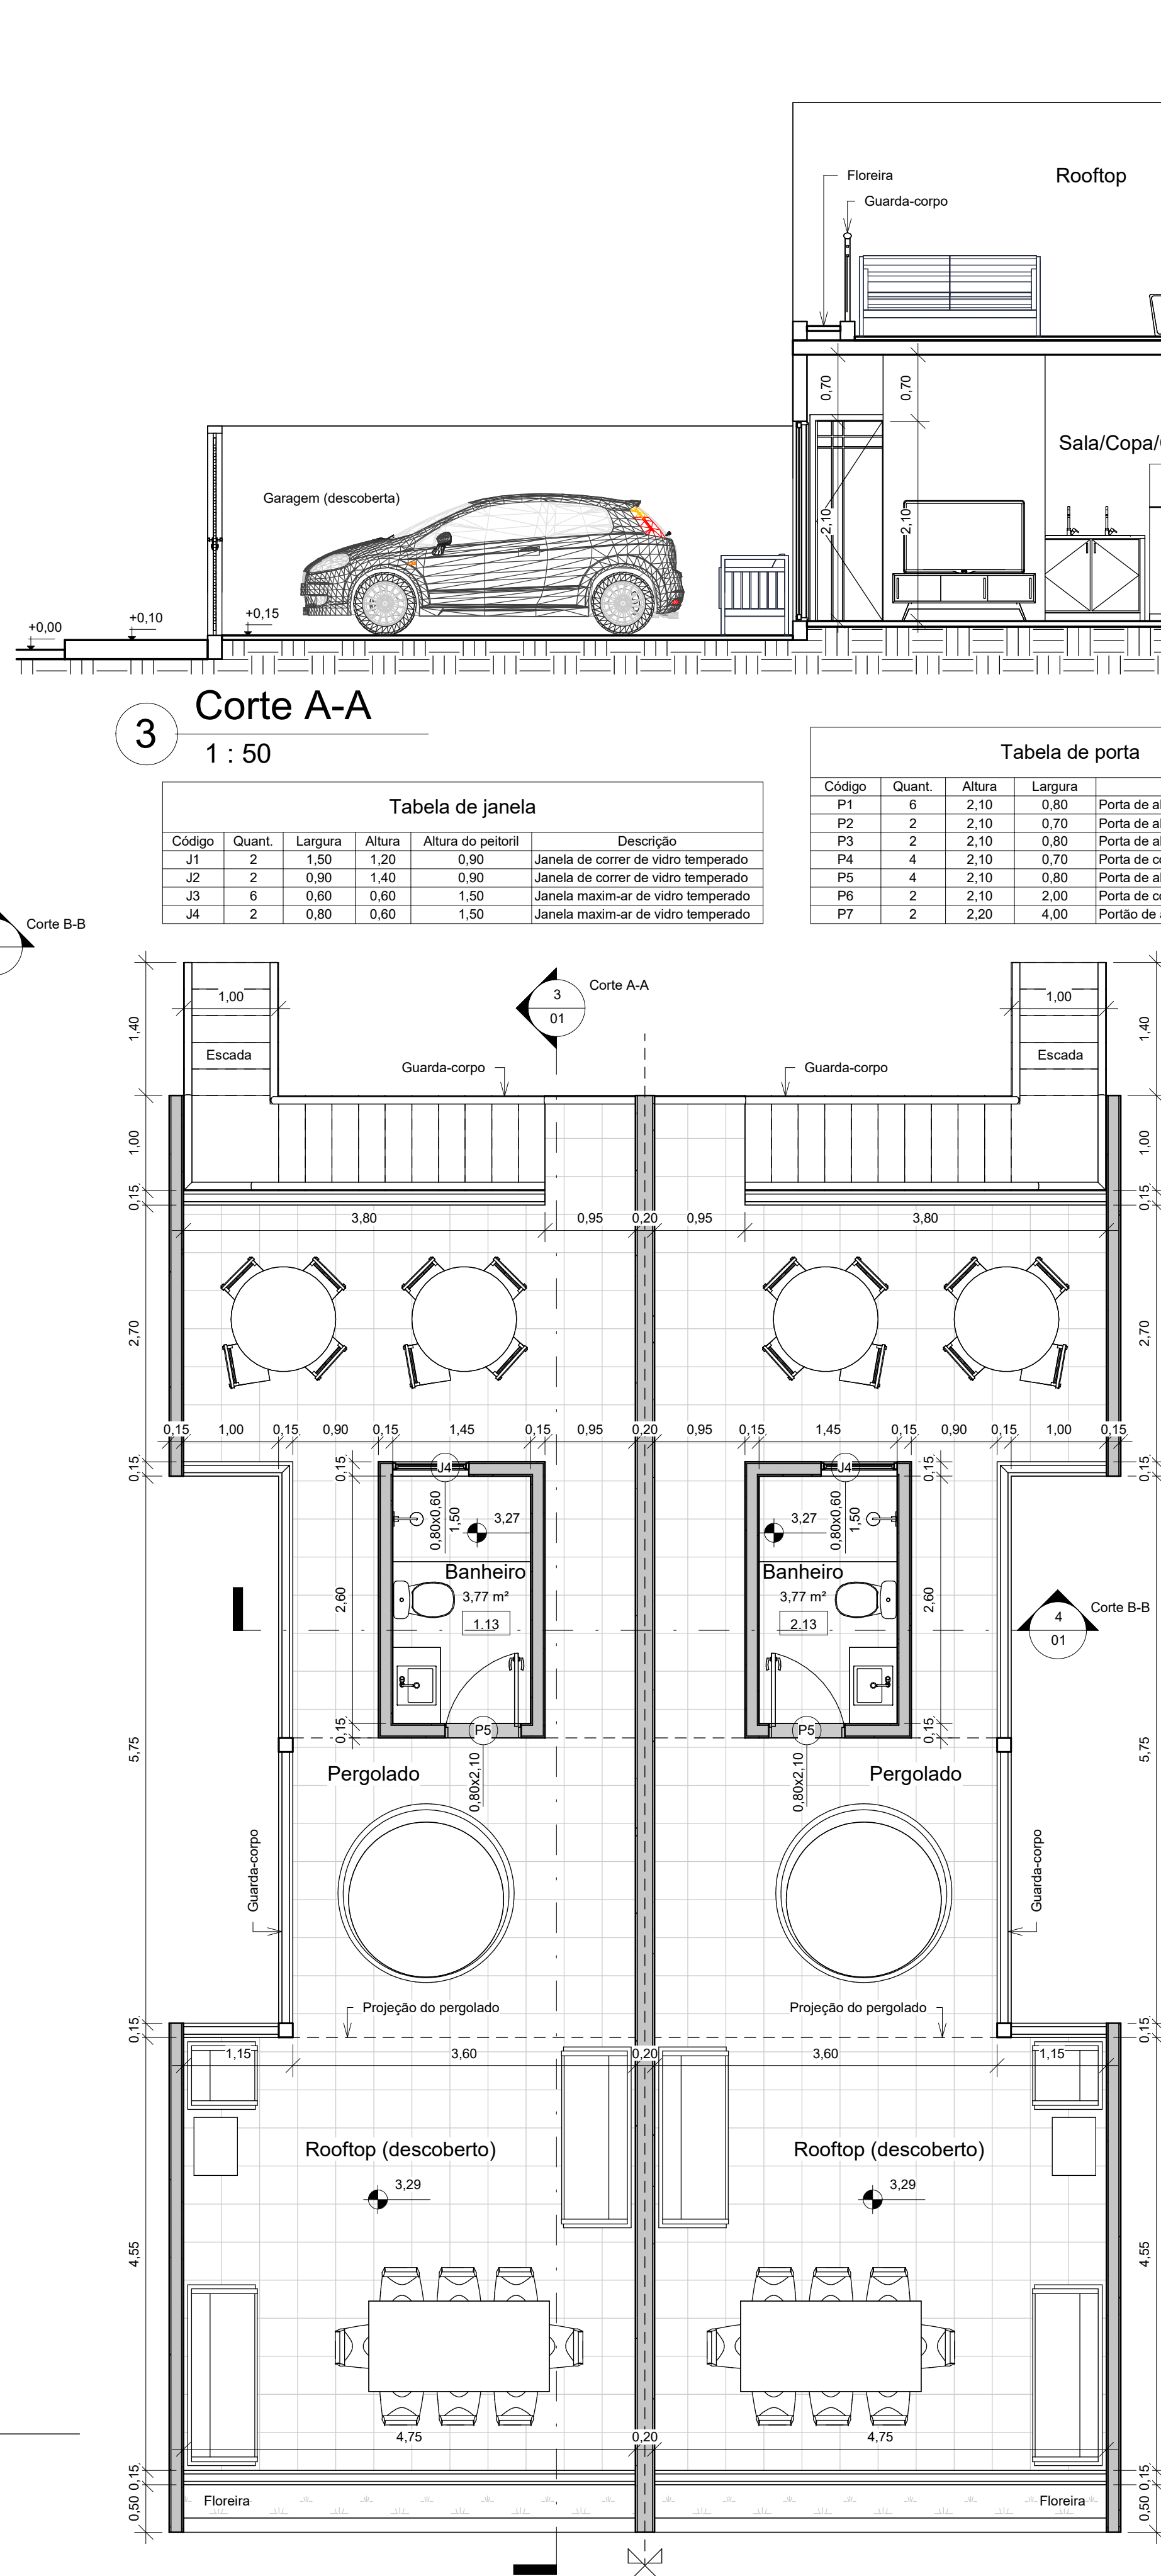


2 Pav. Superior
1 : 50

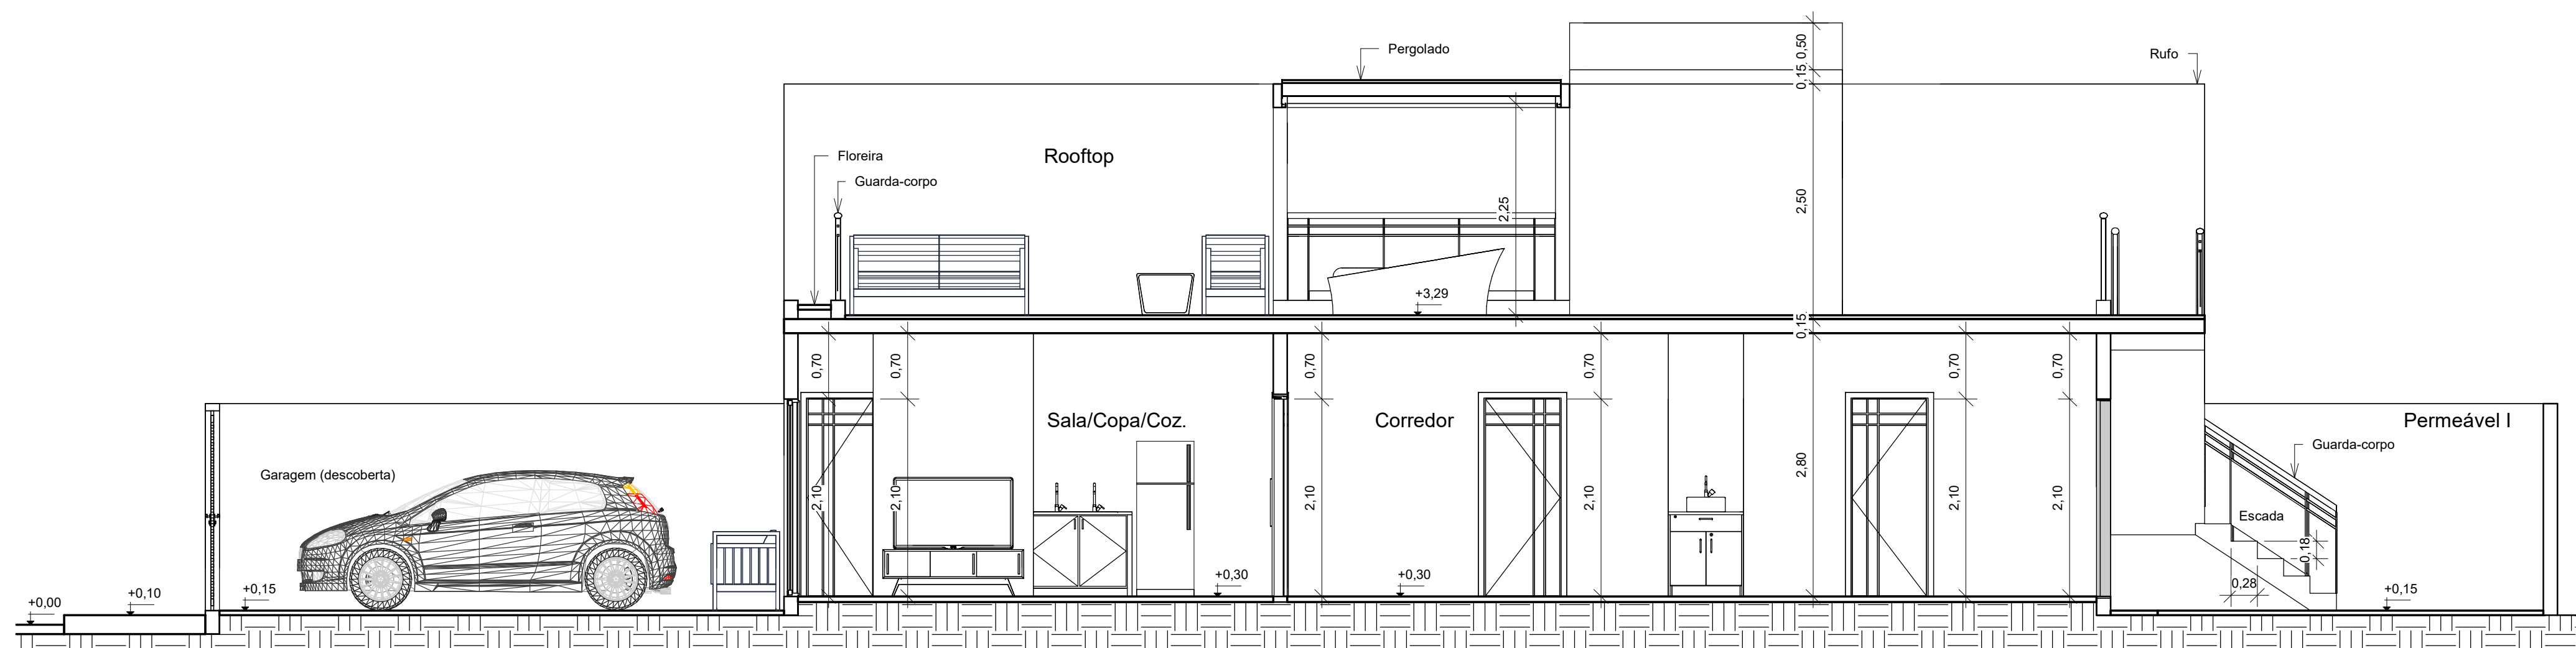


3 Corte A-A
1 : 50

Tabela de janela				
Código	Quant.	Largura	Altura	Altura do peitoril
J1	2	1,50	1,20	0,90
J2	2	0,90	1,40	0,90
J3	6	0,60	0,60	1,50
J4	2	0,80	0,60	1,50

Tabela de porta				
Código	Quant.	Altura	Largura	Descrição
P1	6	2,10	0,80	Porta de abrir de madeira
P2	2	2,10	0,70	Porta de abrir de madeira
P3	2	2,10	0,80	Porta de abrir de vidro temperado
P4	4	2,10	0,70	Porta de correr de vidro temperado
P5	4	2,10	0,80	Porta de abrir veneziana
P6	2	2,10	2,00	Porta de correr de vidro temperado
P7	2	2,20	4,00	Portão de abrir de aço

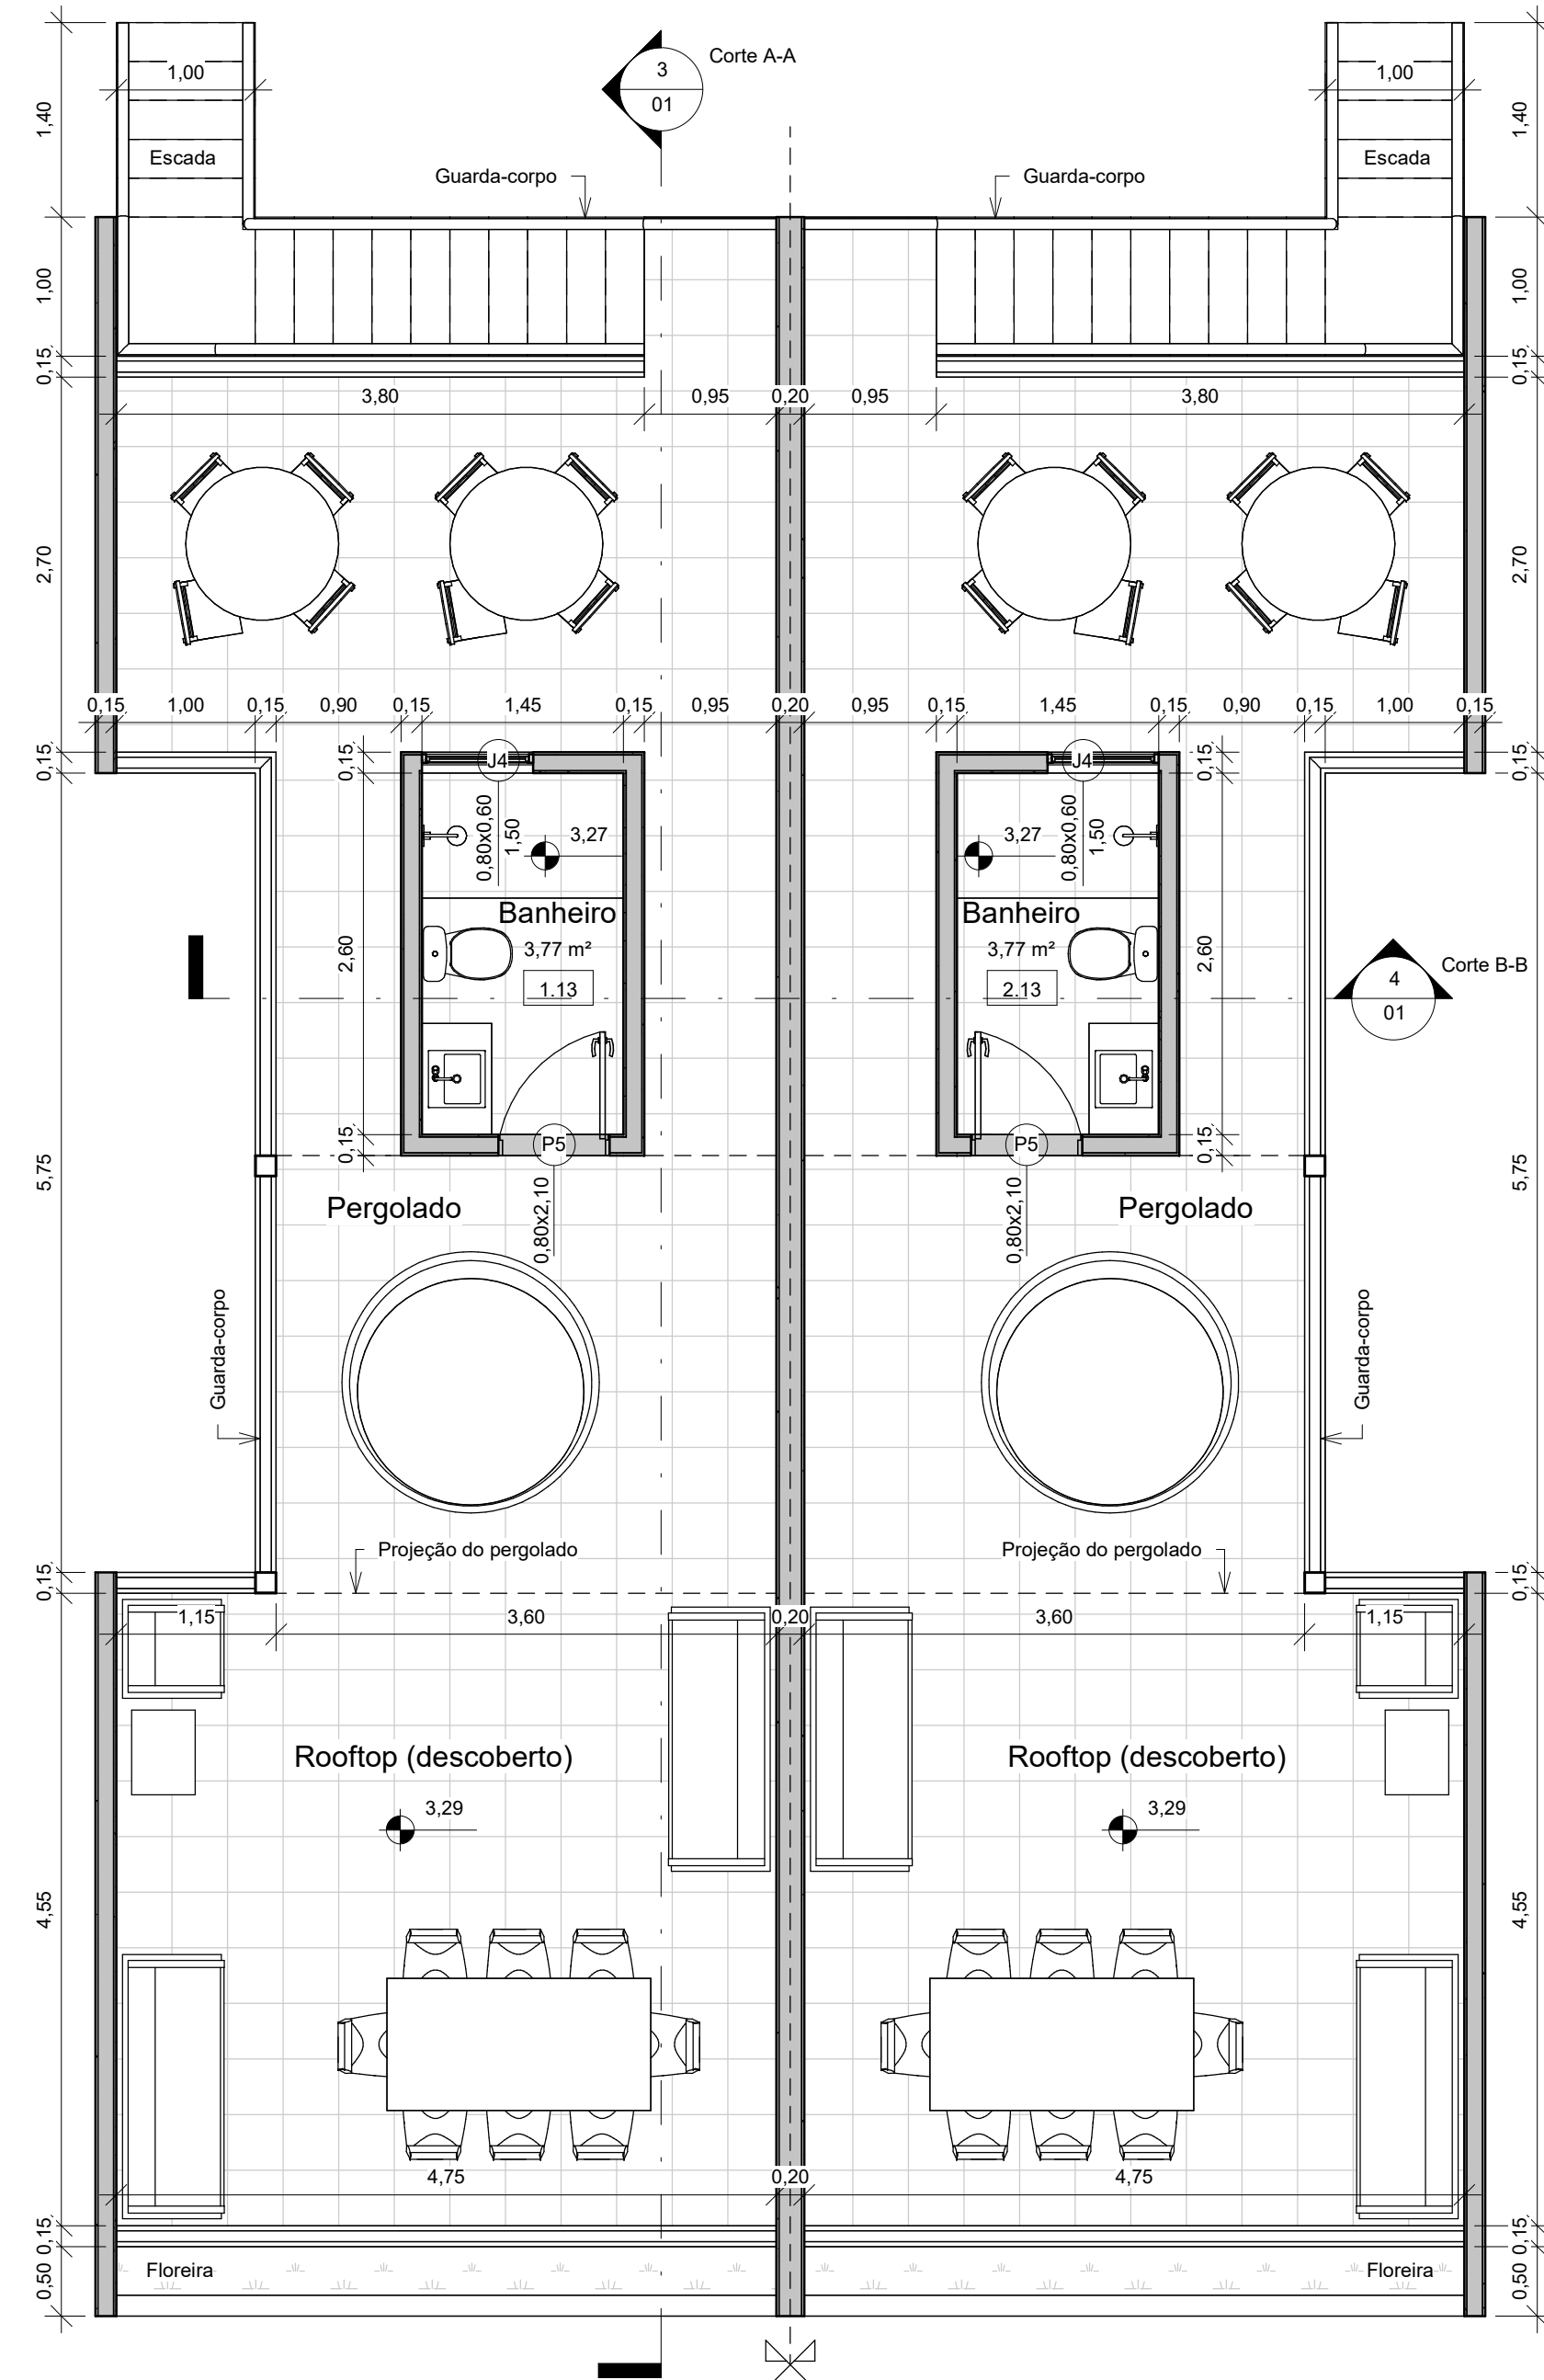


4 Corte B-B
1 : 50

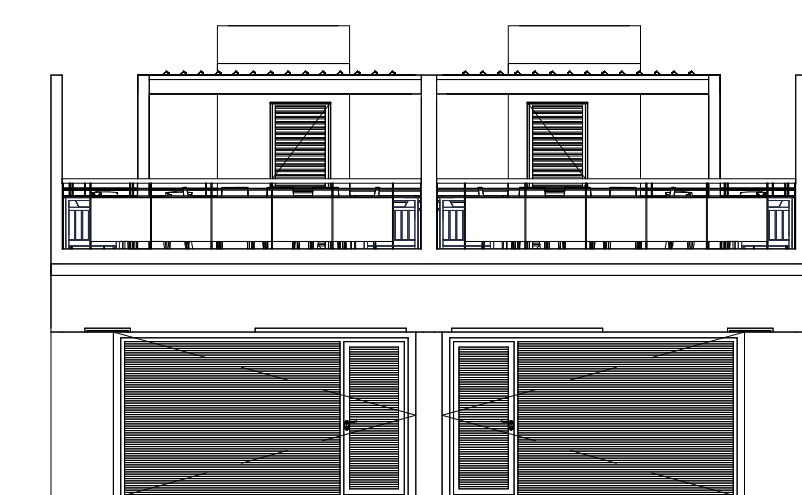

5 Fachada
1 : 100

Tabela de ambiente			
Item	Área	Nome	Nível
1.1	9,86 m²	Quarto 01	Pav. Térreo
1.2	8,17 m²	Corredor	Pav. Térreo
1.3	3,77 m²	Banheiro	Pav. Térreo
1.4	7,50 m²	Quarto 02	Pav. Térreo
1.5	20,28 m²	Sala/Copa/Coz.	Pav. Térreo
1.6	1,68 m²	WC	Pav. Térreo
1.7	1,12 m²	Lavabo	Pav. Térreo
1.8	2,73 m²	Serviço	Pav. Térreo
1.9	19,58 m²	Permeável I	Pav. Térreo
1.10	2,38 m²	Permeável II	Pav. Térreo
1.11	3,00 m²	Permeável III	Pav. Térreo
1.12	3,00 m²	Permeável IV	Pav. Térreo
1.13	3,77 m²	Banheiro	Pav. Superior
2.1	9,86 m²	Quarto 01	Pav. Térreo
2.2	8,17 m²	Corredor	Pav. Térreo
2.3	3,77 m²	Banheiro	Pav. Térreo
2.4	7,50 m²	Quarto 02	Pav. Térreo
2.5	20,28 m²	Sala/Copa/Coz.	Pav. Térreo
2.6	1,68 m²	WC	Pav. Térreo
2.7	1,12 m²	Lavabo	Pav. Térreo
2.8	2,73 m²	Serviço	Pav. Térreo
2.9	19,58 m²	Permeável I	Pav. Térreo
2.10	2,38 m²	Permeável II	Pav. Térreo
2.11	3,00 m²	Permeável III	Pav. Térreo
2.12	3,00 m²	Permeável IV	Pav. Térreo
2.13	3,77 m²	Banheiro	Pav. Superior

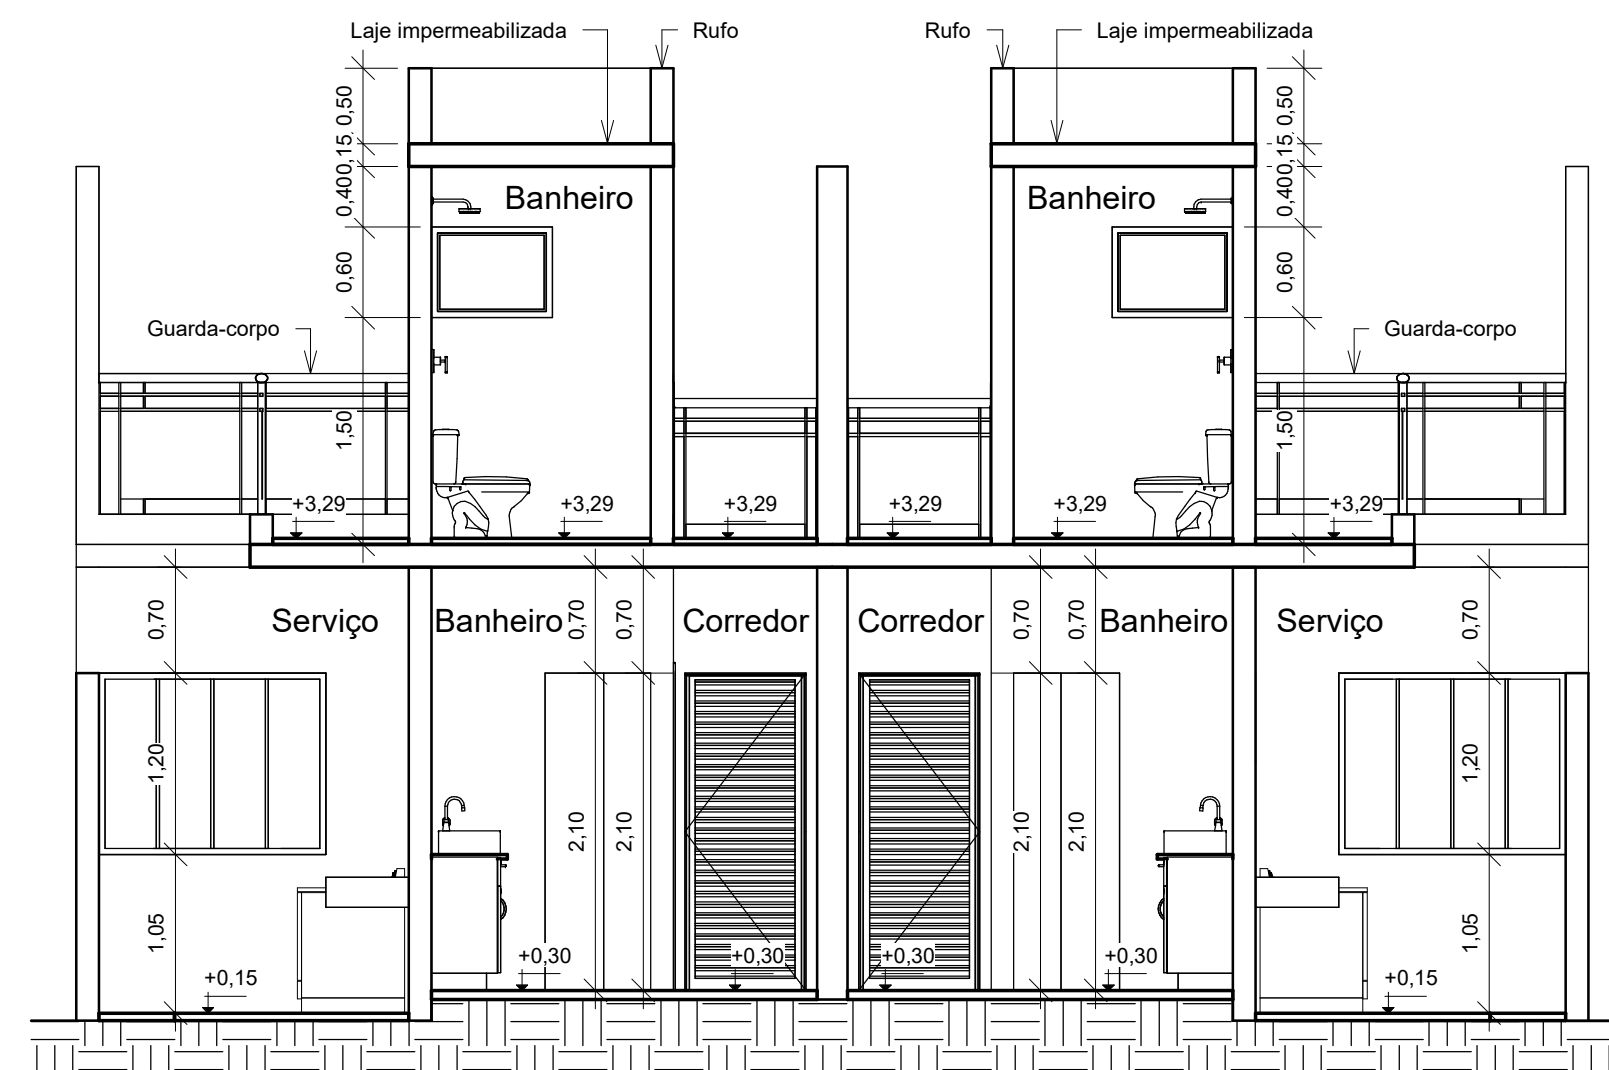

4 Corte B-B
1 : 50

TÍTULO:
PROJETO ARQUITETÔNICO

SUB-TÍTULO:
PROJETO ARQUITETÔNICO RESIDENCIAL MULTIFAMILIAR

DESCRIÇÃO:
PAV. TÉRREO, PAV. SUPERIOR, CORTES, FACHADA, DETALHES E TABELAS.

ENDEREÇO:
RUA ANTÔNIO BORGES CAMPOS (NONINHO), LOTE 03, QUADRA A, RESIDENCIAL MONTE VERDE, CAPETINGA-MG.

FOLHA:
ÚNICA

DATA:
SETEMBRO/2026

ESCALA:
INDICADAS

ART/TRT:

SITUAÇÃO SEM ESCALA:

QUADRO DE ÁREAS

TERRENO	250,00 M² (100,00 %)
PAV. TÉRREO (AP. 01)	63,89 M² (25,56 %)
PAV. SUPERIOR (AP. 01)	5,08 M² (2,03 %)
TOTAL A CONSTRUIR (AP. 01)	68,97 M² (27,59 %)
PAV. TÉRREO (AP. 02)	63,89 M² (25,56 %)
PAV. SUPERIOR (AP. 02)	5,08 M² (2,03 %)
TOTAL A CONSTRUIR (AP. 02)	68,97 M² (27,59 %)
ÁREA PERMEÁVEL TOTAL	55,92 M² (22,37 %)
COEFICIENTE DE APROVEITAMENTO	0,5518
COEFICIENTE DE OCUPAÇÃO	51,11 %

RESPONSÁVEL TÉCNICO:

DENER LOPES SILVA
TÉCNICO EM EDIFICAÇÕES
CPF: 0694162975-7

CONTRATANTE:

DCORP ENGENHARIA
CNPJ: 55.085.352/0001-89

DECLARO QUE A APROVAÇÃO DO PROJETO NÃO IMPLICA A PREFEITURA NO RECONHECIMENTO DE DIREITO DE PROPRIEDADE DO TERRENO. O PROPRIETÁRIO SE COMPROMETE A IMPEDIR QUE AS ÁGUAS PLUVIAIS SEJAM LANÇADAS NA REDE DE ESGOTO.

APROVAÇÕES:

DCORP ENGENHARIA
Dener L. Rendal
Construção industrializada com propósito

(19) 99367-0722
dener@dcorp.com.br
www.dcorp.com.br